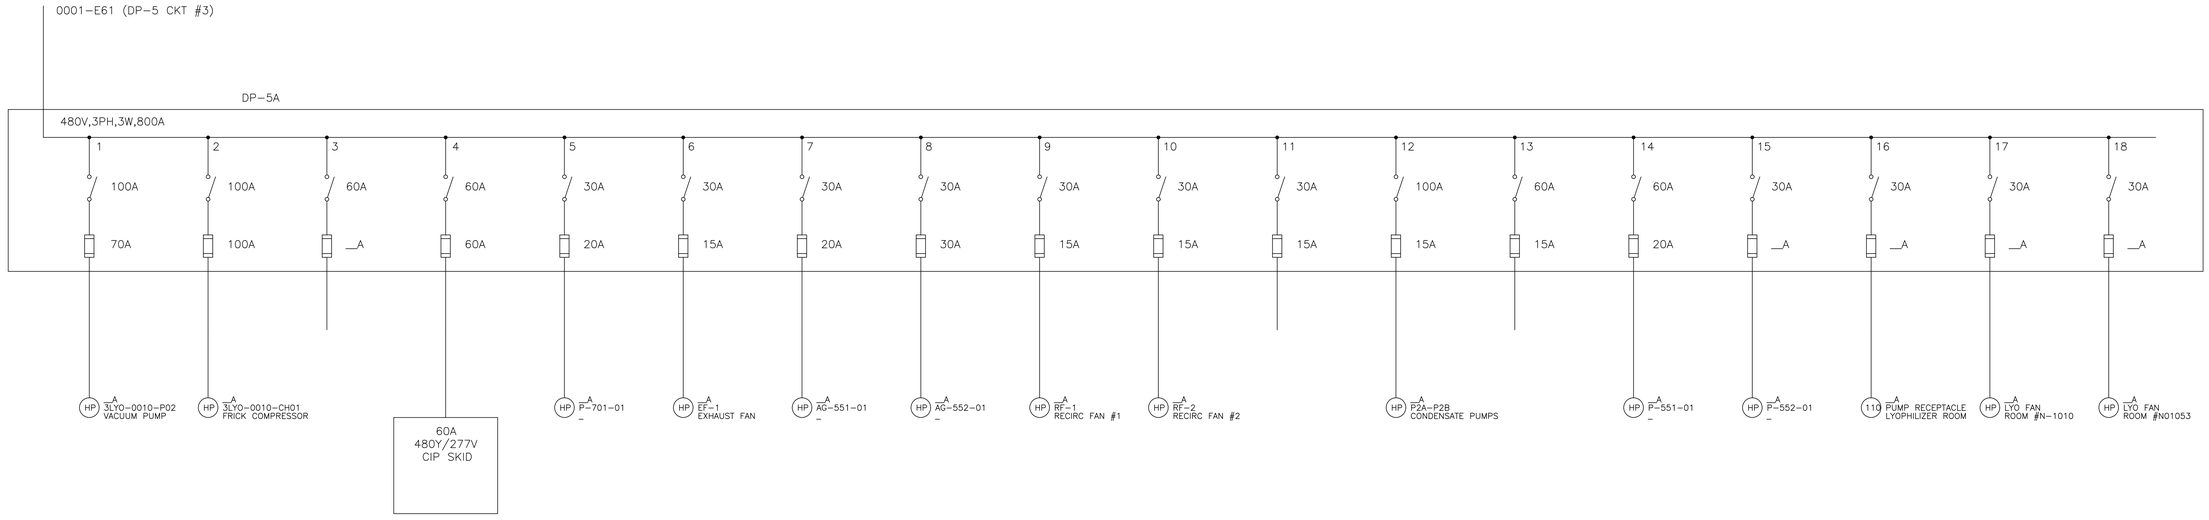


NO	REVISIONS	APPROVED	DATE
–	–	–	–
2	REVISED PER PROJECT#11-017 MOC#0272	SG/TP	10/18/11
1	REVISED PER PROJECT#11-017 MOC#10000007397-20160	SG/TP	04-26-11

SIGMA-ALDRICH

TITLE: N BUILDING DEVELOPMENT
DP-5A ELECTRICAL ROOM #1023
ONE-LINE DIAGRAM

SITE: CHEROKEE BLDG: N FLOOR: 1ST

SCALE:	DRAWN: RGF	DATE: 04-26-11	DWG NO:
NONE	APPROVED: SG	DATE: 04-26-11	0001-E64