
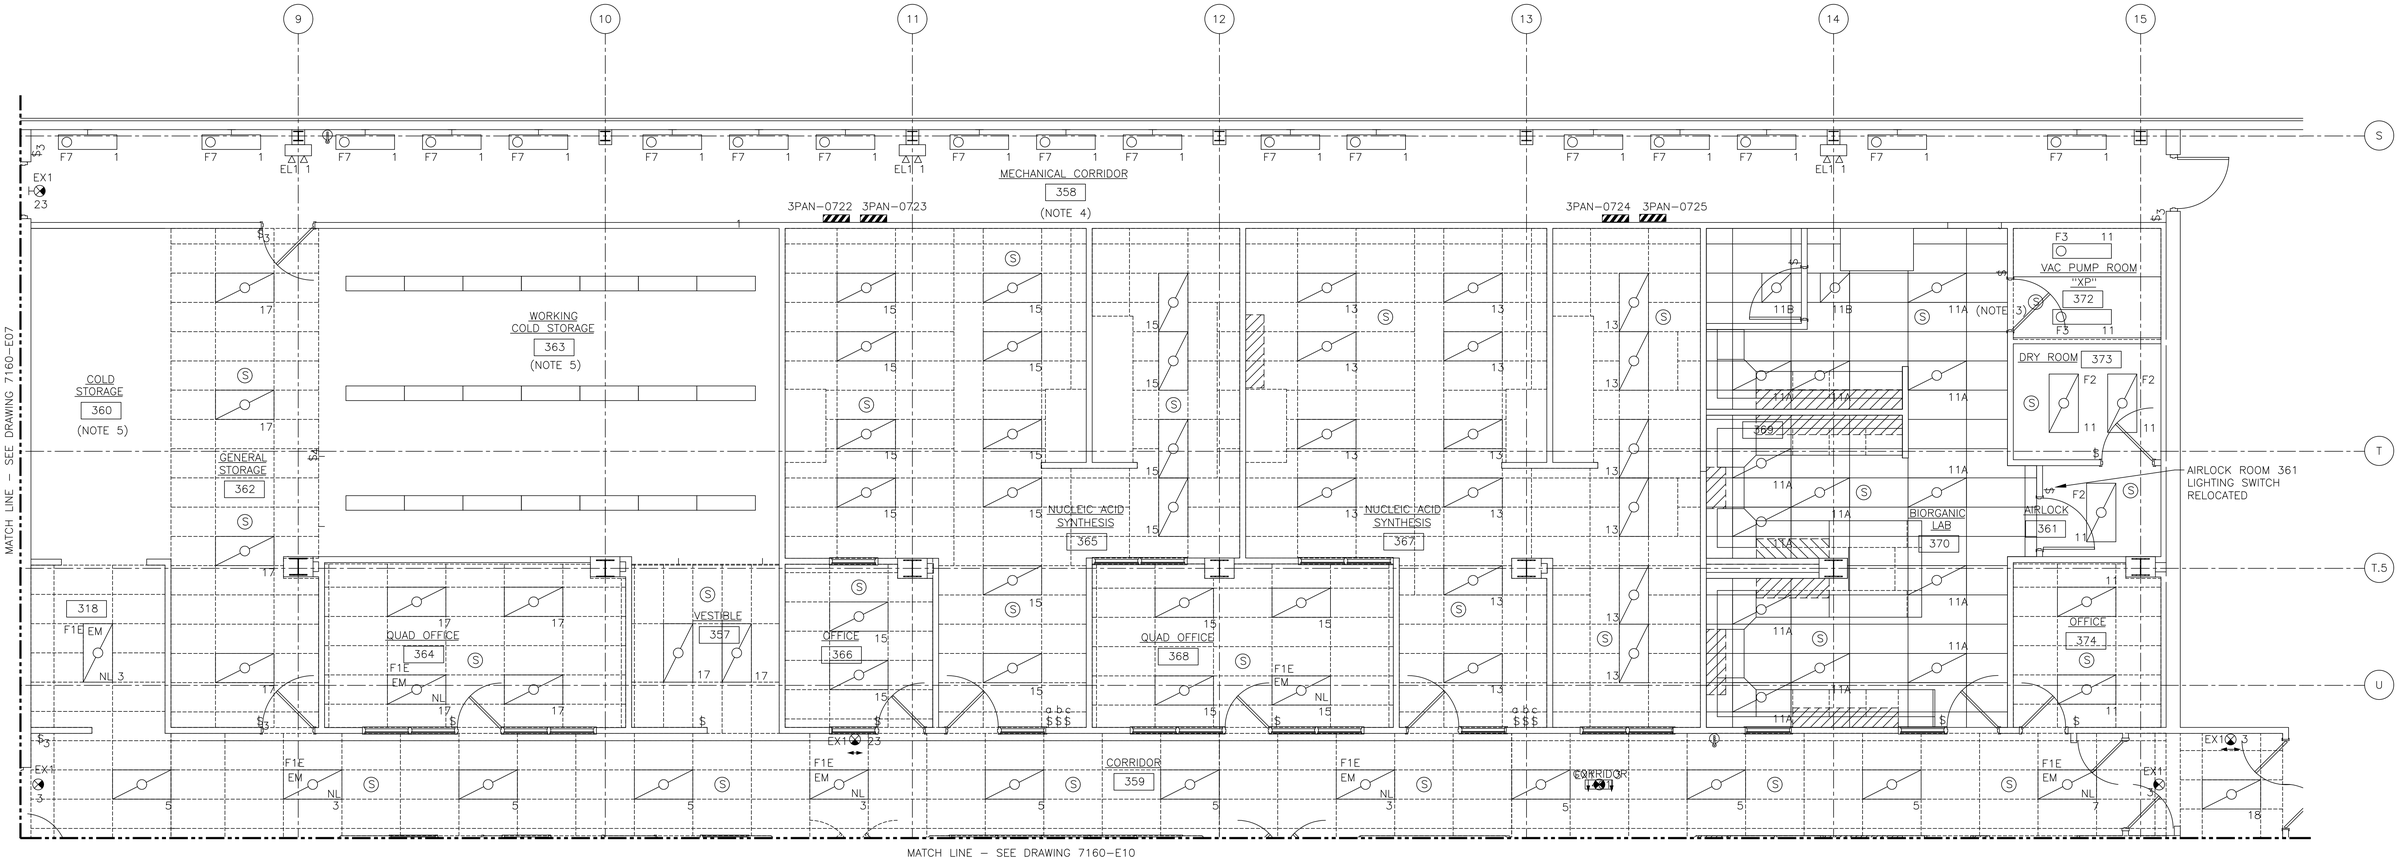


THIRD FLOOR AREA 3 PLAN

1/4" = 1'–0"

NOTES:

1. LIGHTING FIXTURES SHALL BE TYPE 'F1' UNLESS NOTED OTHERWISE.
2. EACH LIGHTING CIRCUIT ON THIS DRAWING SHALL BE FED FROM PANEL 3PAN–0706.
3. ROOM 372 IS CLASSIFIED CLASS 1, GROUP D, DIVISION 2
4. MOUNTING HEIGHT OF LIGHT FIXTURES: 8'–0" AFF.

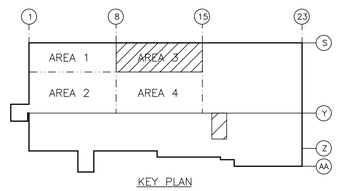

KEY PLAN

0 4 8 12
1/4"=1'–0"

NORTH

OLD 7160-E09

CONSULTING ENGINEERS, INC.
11701 BORMAN DRIVE
SUITE 175
ST. LOUIS, MISSOURI 63146
PH. 314–997–1515
FAX: 314–997–6117
PN: 076416.01

LOCKWOOD GREENE
Consulting • Design • Construction
ST. LOUIS, MISSOURI

NO	REVISIONS	APPROVED	DATE
1	AS DOCUMENTED	DSH	02–09–01
0	INITIAL ISSUE	JLS	04–20–00

DEPARTMENT FOR	DESIGN APPROVALS INITIAL	DATE
REVIEW		
COMPLIANCE		
DEPARTMENTS		
ENGINEERING		
MAINTENANCE		
SAFETY		

SIGMA-ALDRICH CORPORATION

TITLE:
"N" BUILDING DEVELOPMENT
ELECTRICAL
LIGHTING PLAN - THIRD FLOOR

PLANT: CHEROKEE BLDG: "N" FLOOR: 3RD
DRAWN: WHW/RLH SCALE: 1/4"=1'–0" DATE: 04–03–00
CHECKED: gwg APPROVED: JLS DATE: 04–20–00

0001-E09

Drawing File = r:\bc-workspace\s11868#\m-osti1-w0002_d-sigmarch\ref\sigmabdr.dwg
Plotted at 12:39pm on Nov 30, 2022 by S118688